




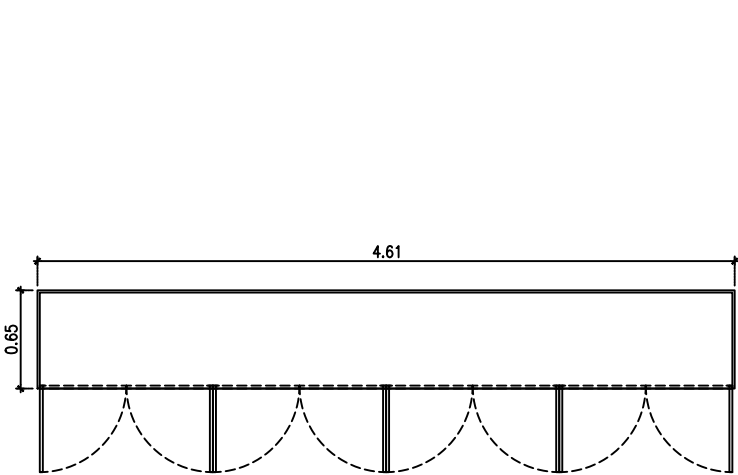

1 PLANTA  
SOTANO 1:50

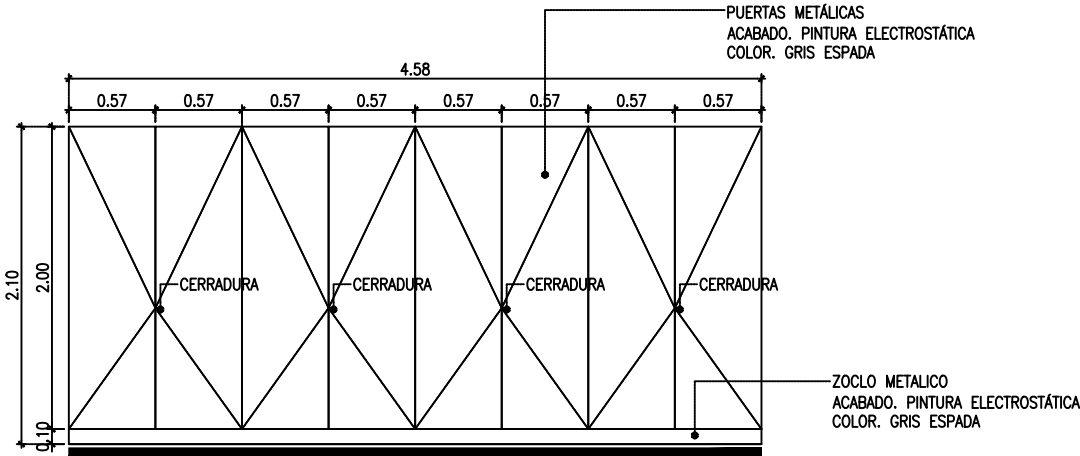

2 ALZADO  
SOTANO 1:50

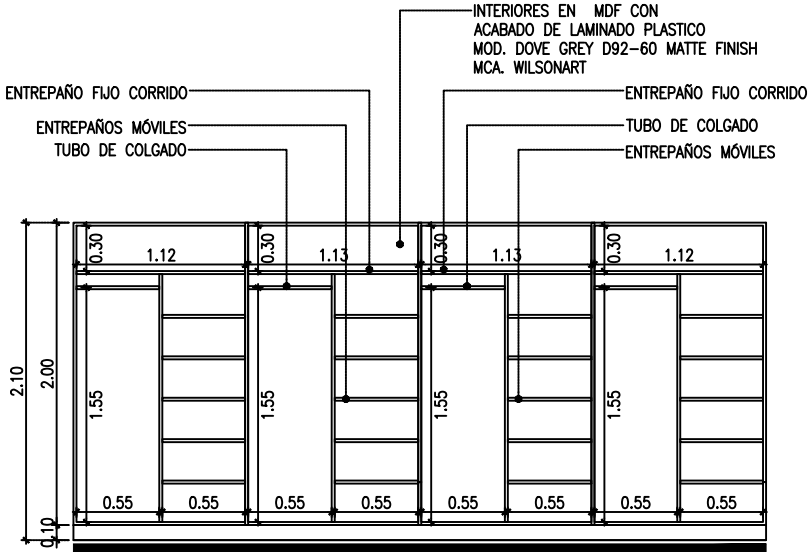

2 INTERIOR  
SOTANO 1:50

CONTRATISTA GENERAL

GIA

ADAPTACION DE DISEÑO



SERRANO +

JUAN PABLO SERRANO OROZCO

C. 18 254, Carola, San Pedro de los Pinos,  
Álvaro Obregón, 01180 Ciudad de México,  
CDMX

CLIENTE

BBVA

PROYECTO


BBVA – PRÁDO NORTE – S1

UBICACIÓN

Avenida Paseo de la Reforma 305

NIVEL S3

LOCALIZACIÓN

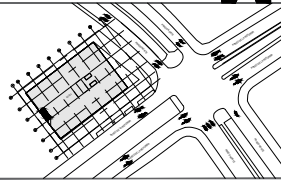

NOTAS – CLAVES – SIMBOLOGÍA

NOTAS GENERALES

- COTAS EN METROS; RIGEN EL DIBUJO Y NO SE TOMARAN MEDIDAS A ESCALA DE ESTE PLANO.
- EL CONTRATISTA RECTIFICARA EN EL LUGAR DE LA OBRA LAS DIMENSIONES Y NIVELES INDICADOS EN ESTE PLANO ANTES DE EJECUTAR CUALQUIER TRABAJO, DEBIENDO SOMETER A LA DIRECCIÓN DE LA OBRA CUALQUIER DIFERENCIA QUE HUBIERE ASI COMO LA INTERPRETACION QUE DE EL PROPIO CONTRATISTA A ESTE DIBUJO.
- ESTE PLANO DEBERA VERIFICARSE CON LOS CORRESPONDIENTES DE ESTRUCTURA E INSTALACIONES, CUALQUIER DISCREPANCIA DEBERA CONSULTARSE CON EL PROYECTISTA.
- EL PLANO CON LA ULTIMA CORRECCION CANCELA LA ANTERIOR, LA FECHA RIGE EL ORDEN.
- TODOS LOS ACABADOS, ESPECIFICACIONES Y DETALLES SEÑALADOS EN ESTE PLANO DEBERAN EJECUTARSE DE ACUERDO A LAS ESPECIFICACIONES.
- PLANOS ARQUITECTONICOS MANDAN A CUALQUIER INSTALACION Y ESTRUCTURA.

ARCHIVO

BBVA WP S3 I-7.R5.DWG

PLANO

CLOSET

FECHA

22.06.2026

ACOTACIÓN

METROS

ESCALA

1:50

CLAVE

S3 | 7 04