



CLIENTE



banco multiva


PROYECTO CORPORATE OFFICES
(MEXICO)

DIRECCIÓN


CROQUIS DE LOCALIZACIÓN

SIMBOLOGÍA

MARCA: LUFT
PROVEEDOR: Rodrigo De La Torre
CONTACTO: 55 4421 0334
rodrigodt@luft.eu

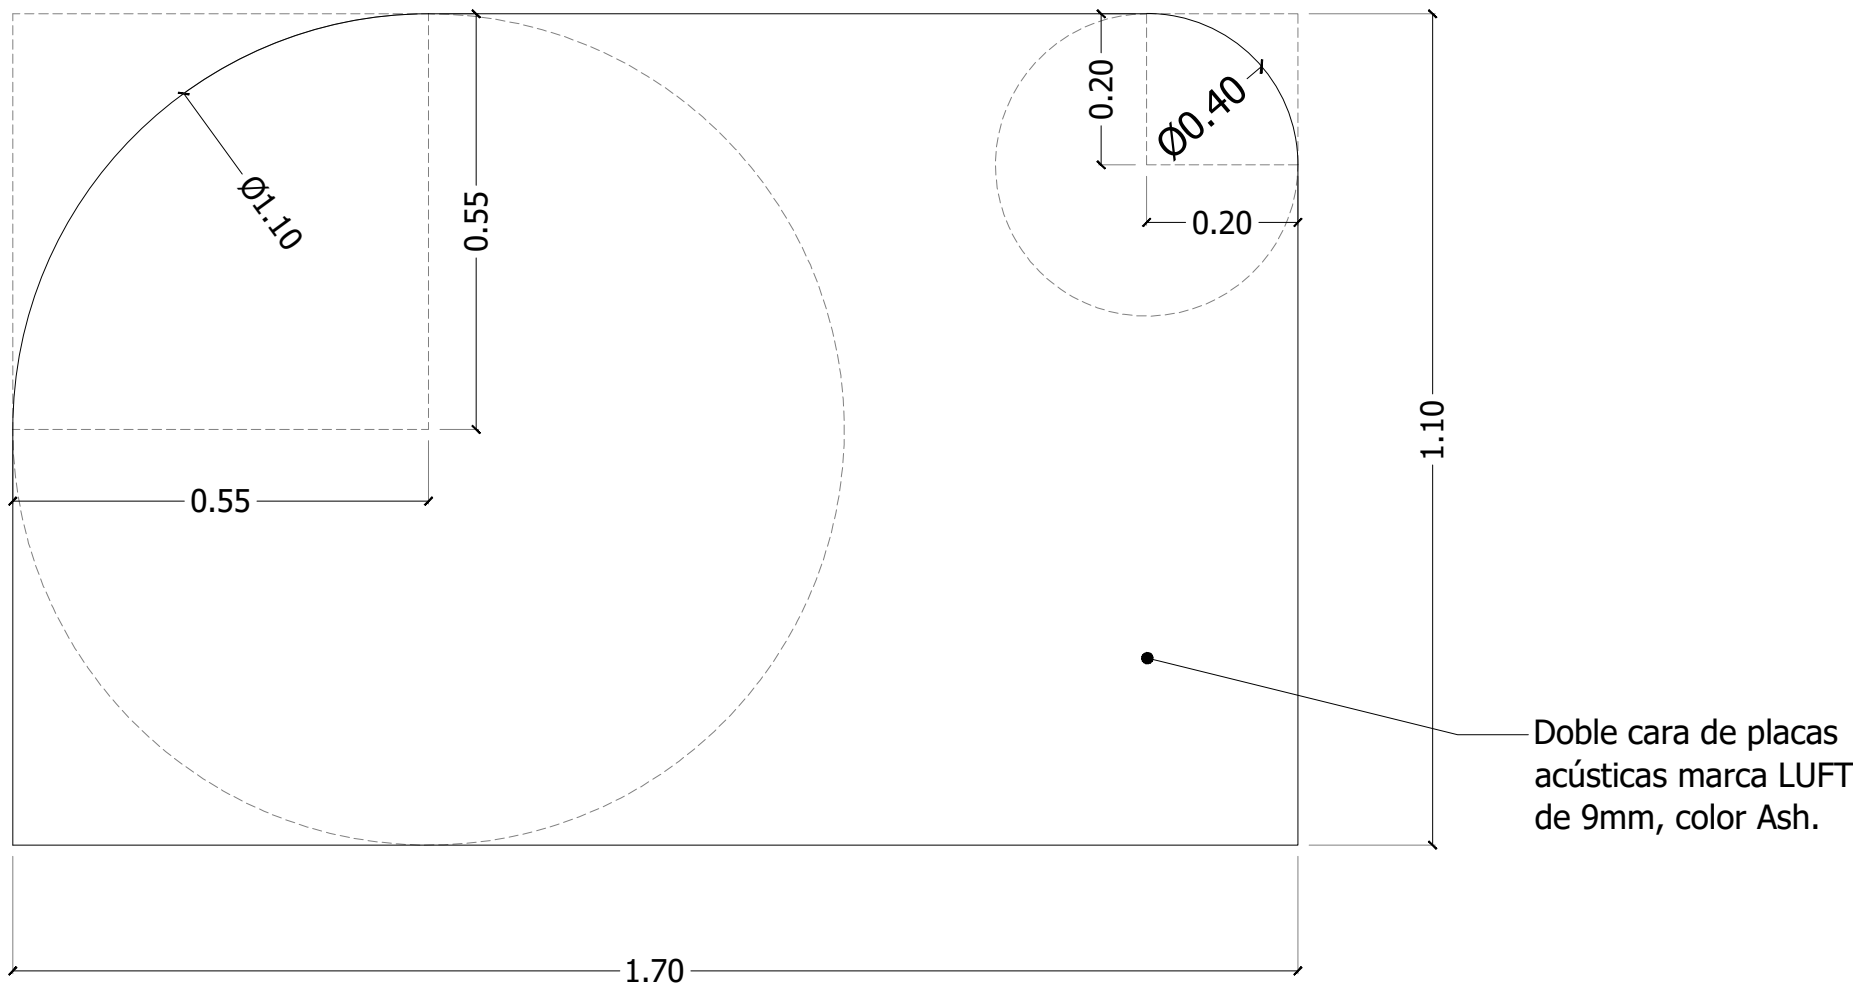

Detalle de Mampara divisoria
(corte de acústico)
Esc 1:25. Unidades en cm.

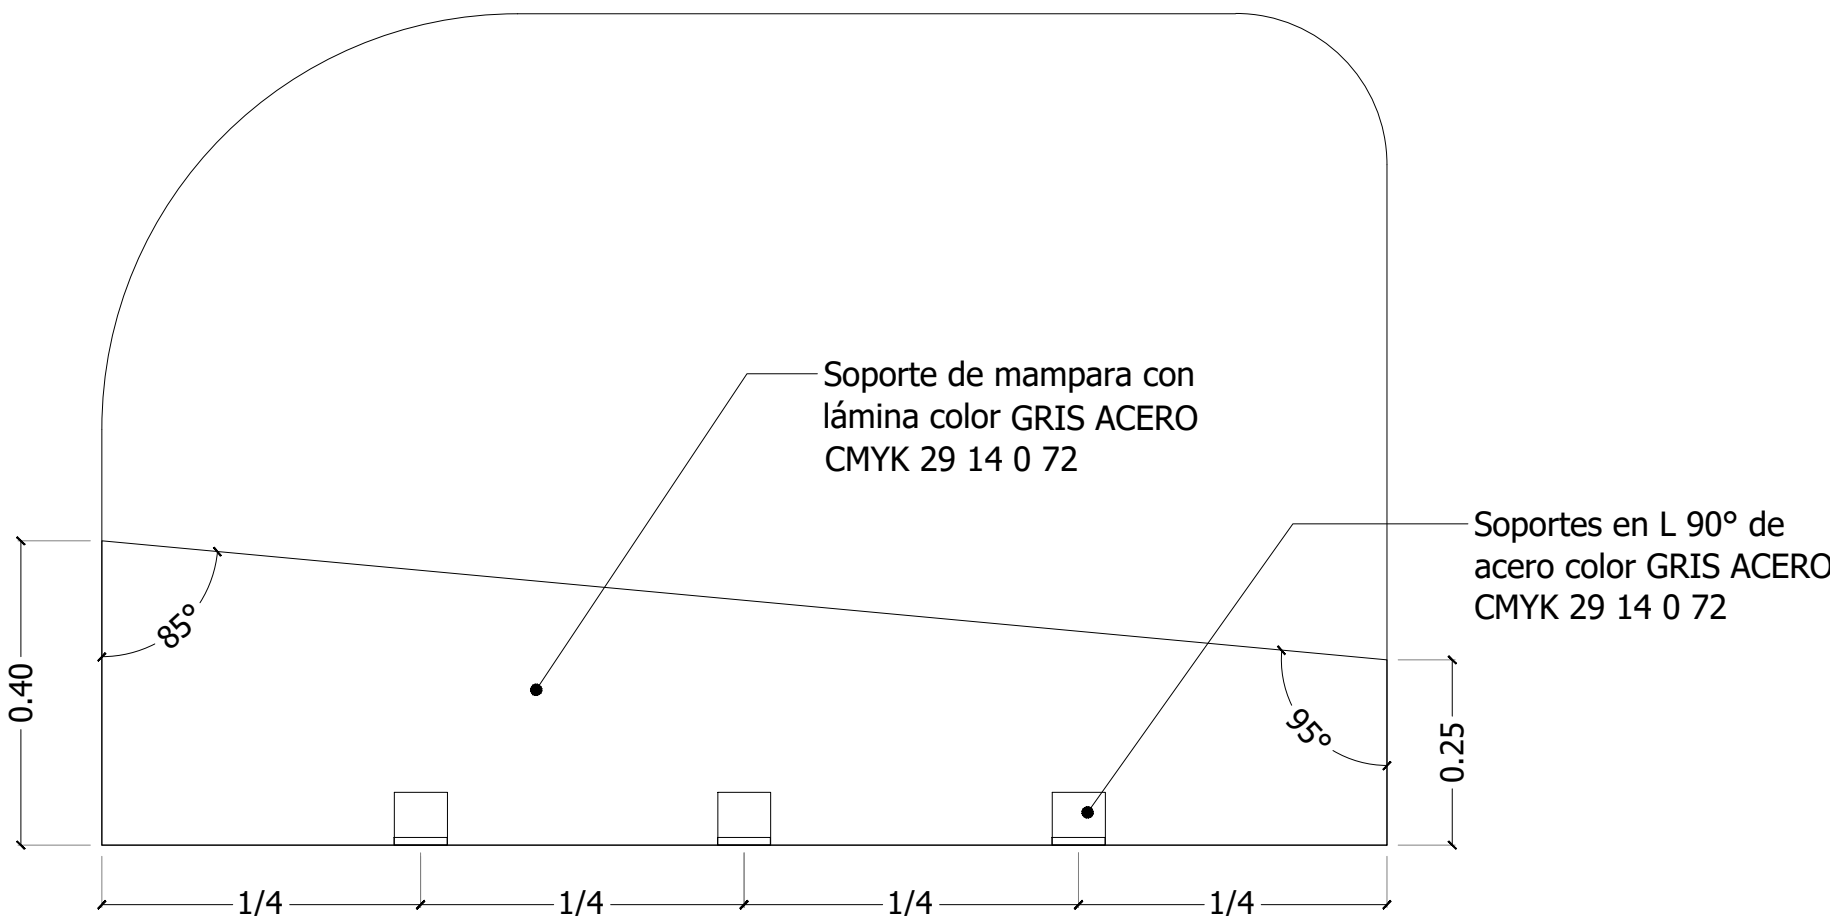

Detalle de Mampara divisoria
(alzado)
Esc 1:25. Unidades en cm.

MVS

PLANO DETALLE DE MAMPARA

FECHA Junio 2025

ESCALA 1:10

UNIDADES m

CLAVE A-352

NOTA Las cotas rigen el plano.
Cualquier discrepancia en planos,
consultar con TRAZO. Este plano
anula a los de fechas anteriores.

VERSIONES

VERSIÓN	FECHAS	NOTAS



CDMX
GAL MOLINO DEL CAMPO 23
SAN MIGUEL CHAPULTEPEC
11850 CDMX
T 55 1198 1538 / 55 1998 1539

www.trazo.com.mx