
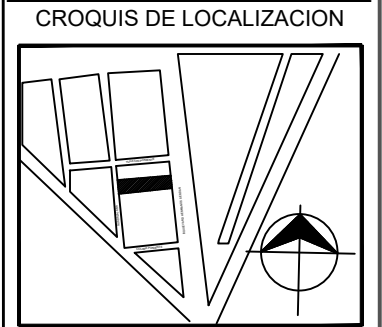
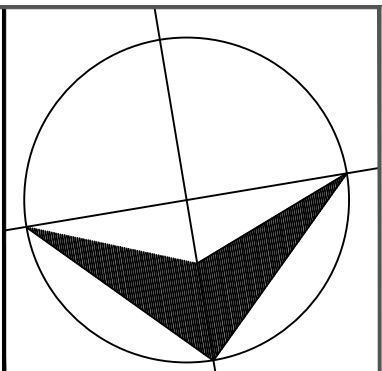


PLANTA ARQUITECTONICA 1ER NIVEL ESC.: 1:75

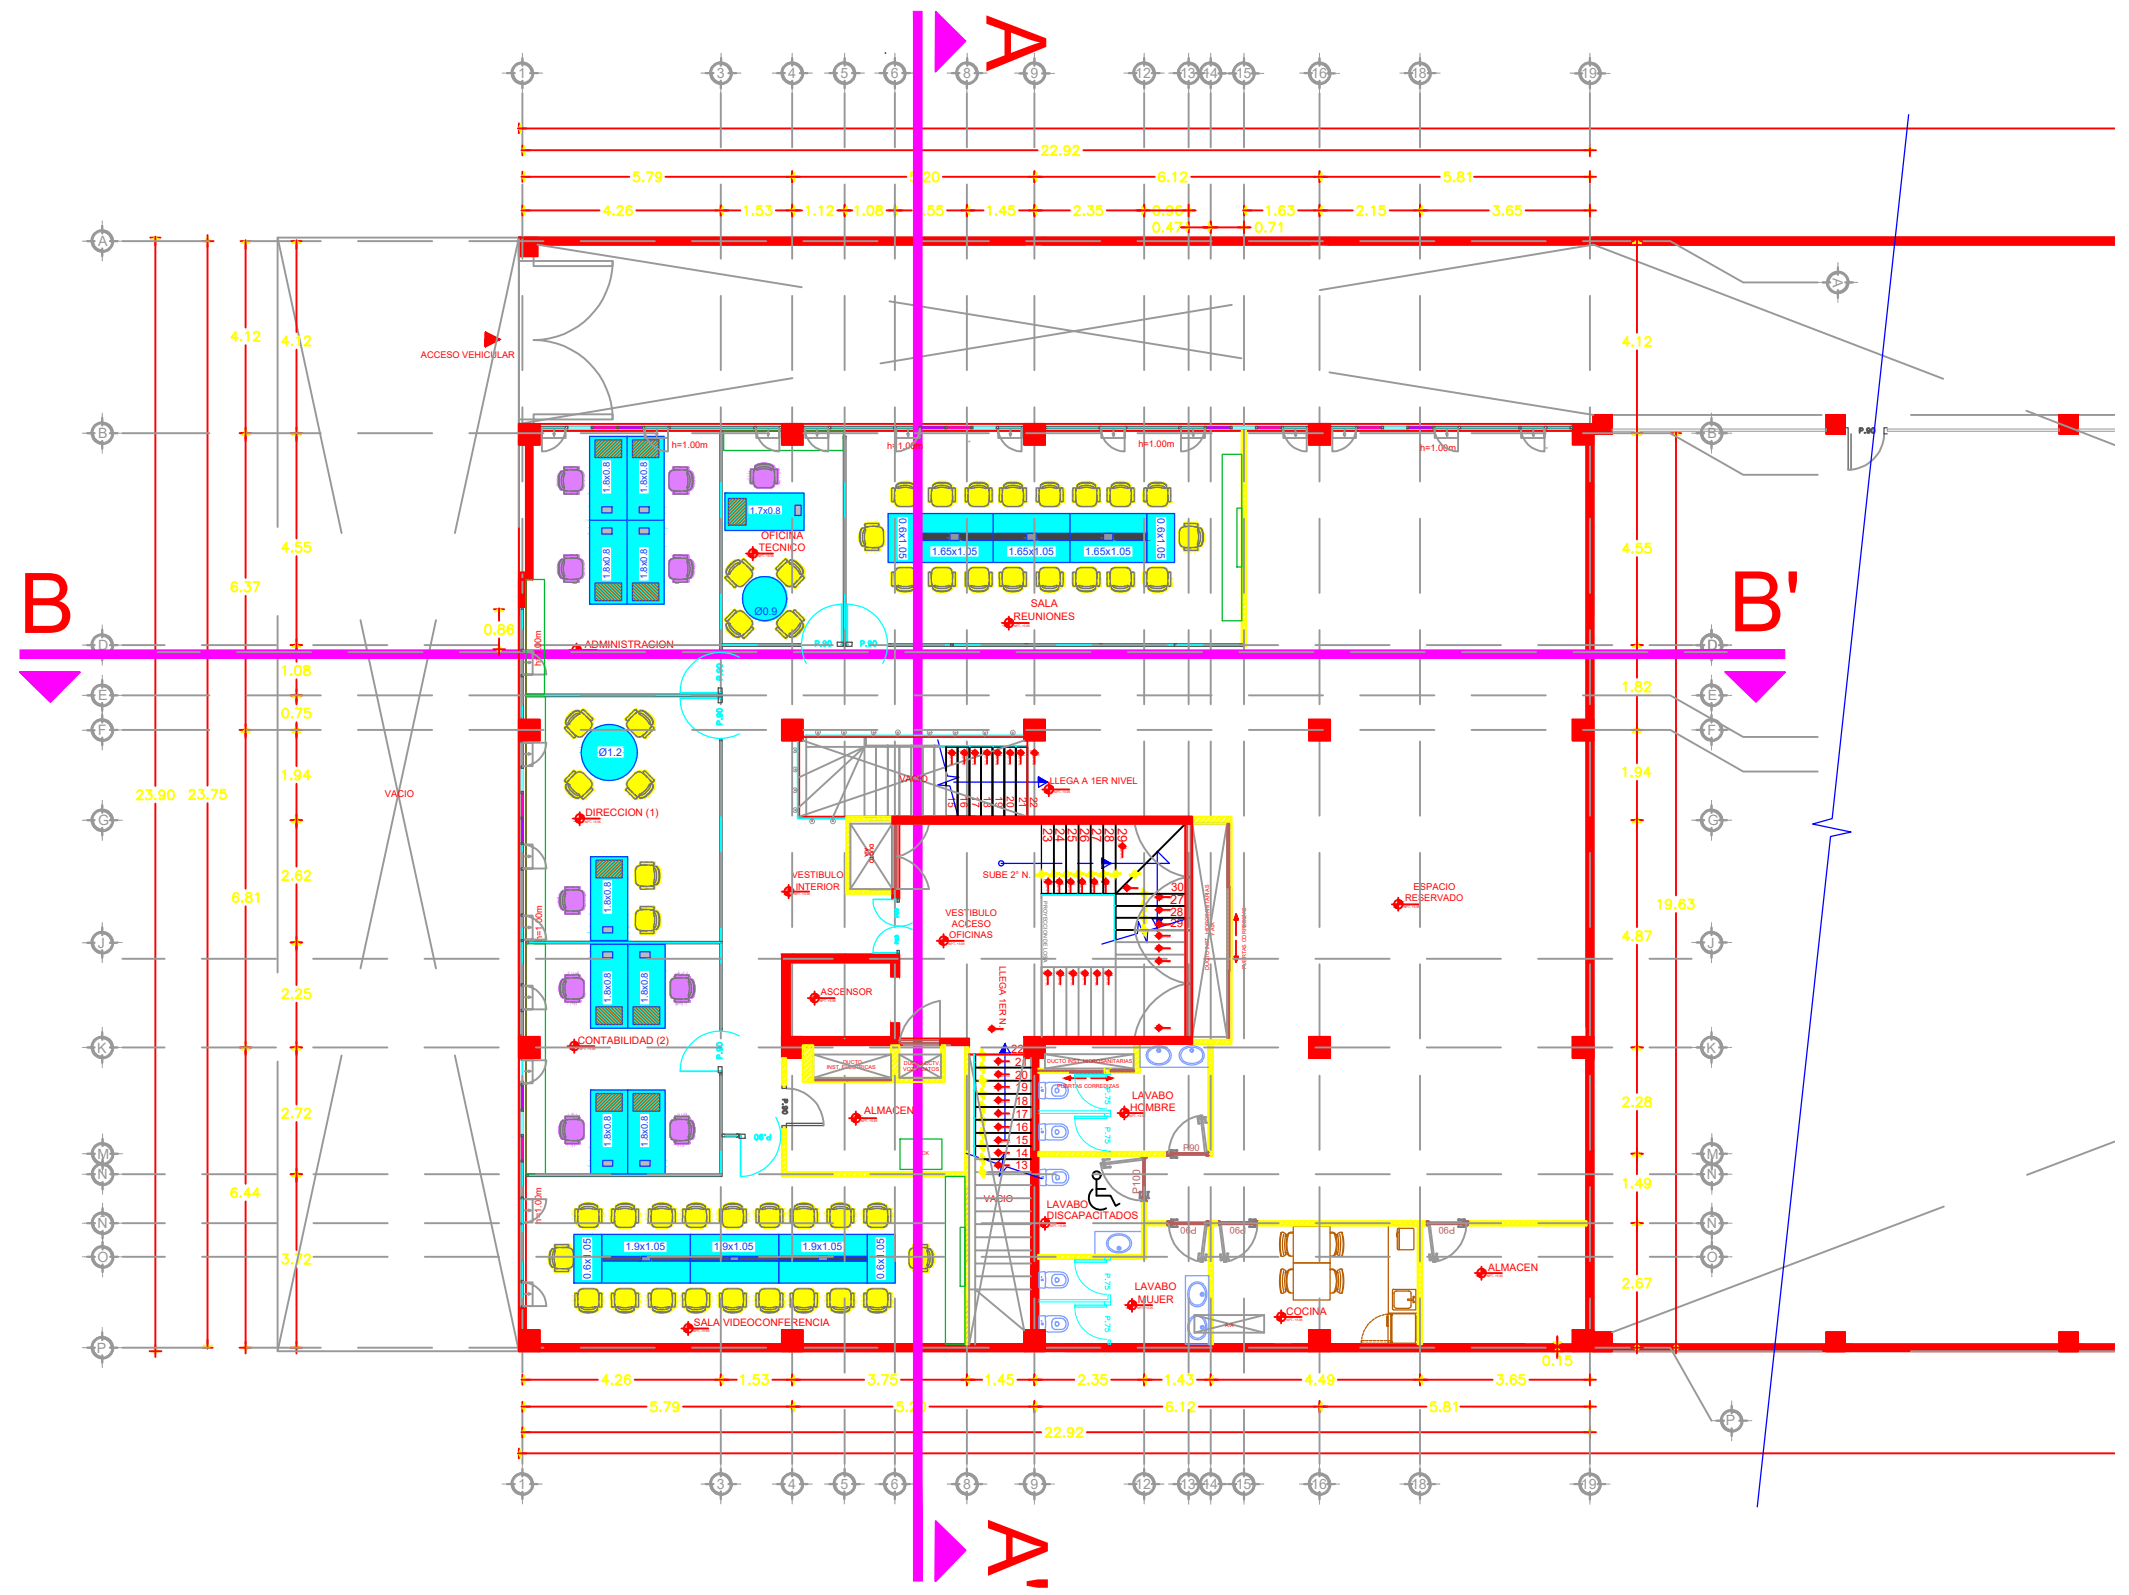

Datos del predio

Cuenta predial:	PU-296784-1
No. de lote:	Lote 2, Manzana 18, Zona 9

- ANOTACIONES
- Pendiente 2 %
 - Cambio de nivel.
 - Nivel de piso terminado.
 - BAP
 - Muro de tablaroca.
 - Herrería.
 - Proyecciones.

CUADRO DE AREAS

SUPERFICIE DE TERRENO	2023.00 m²
SUPERFICIE DE CONSTRUCCION P.B.	459.09 m²
SUPERFICIE DE CONSTRUCCION 1er N.	459.09 m²
SUPERFICIE DE CONSTRUCCION 2º N.	459.09 m²
SUPERFICIE DE CONSTRUCCION 3er N.	459.09 m²
SUPERFICIE DE CONSTRUCCION 4º N.	386.99 m²
SUPERFICIE DE CONSTRUCCION AZOTEA.	45.39 m²
SUPERFICIE DE CONSTRUCCION BODEGA.	811.63 m²
SUPERFICIE TOTAL CONSTRUIDA	3080.37 m²
SUPERFICIE SIN CONSTRUIR	752.28 m²

PROYECTO:
CONSTRUCCION DE OFICINAS SALERM

PROPIETARIO:
FERPE SALON, S.A. DE C.V.

UBICACION:
BOULEVARD HERMANOS SERDAN
No. 663, COL. SAN RAFAEL ORIENTE

SELLOS DE APROBACION:

D.R.O. REGISTRO:

LOCALIZACION:
PUEBLA, PUEBLA

DIBUJO:
ARQ. HECTOR M. MORALES ARANGO

PLANOS:
ARQUITECTONICOS

FECHA: 08/12/2025

MEDIDA: METROS

ESCALA: 1:75

PLANTAS ARQ-02